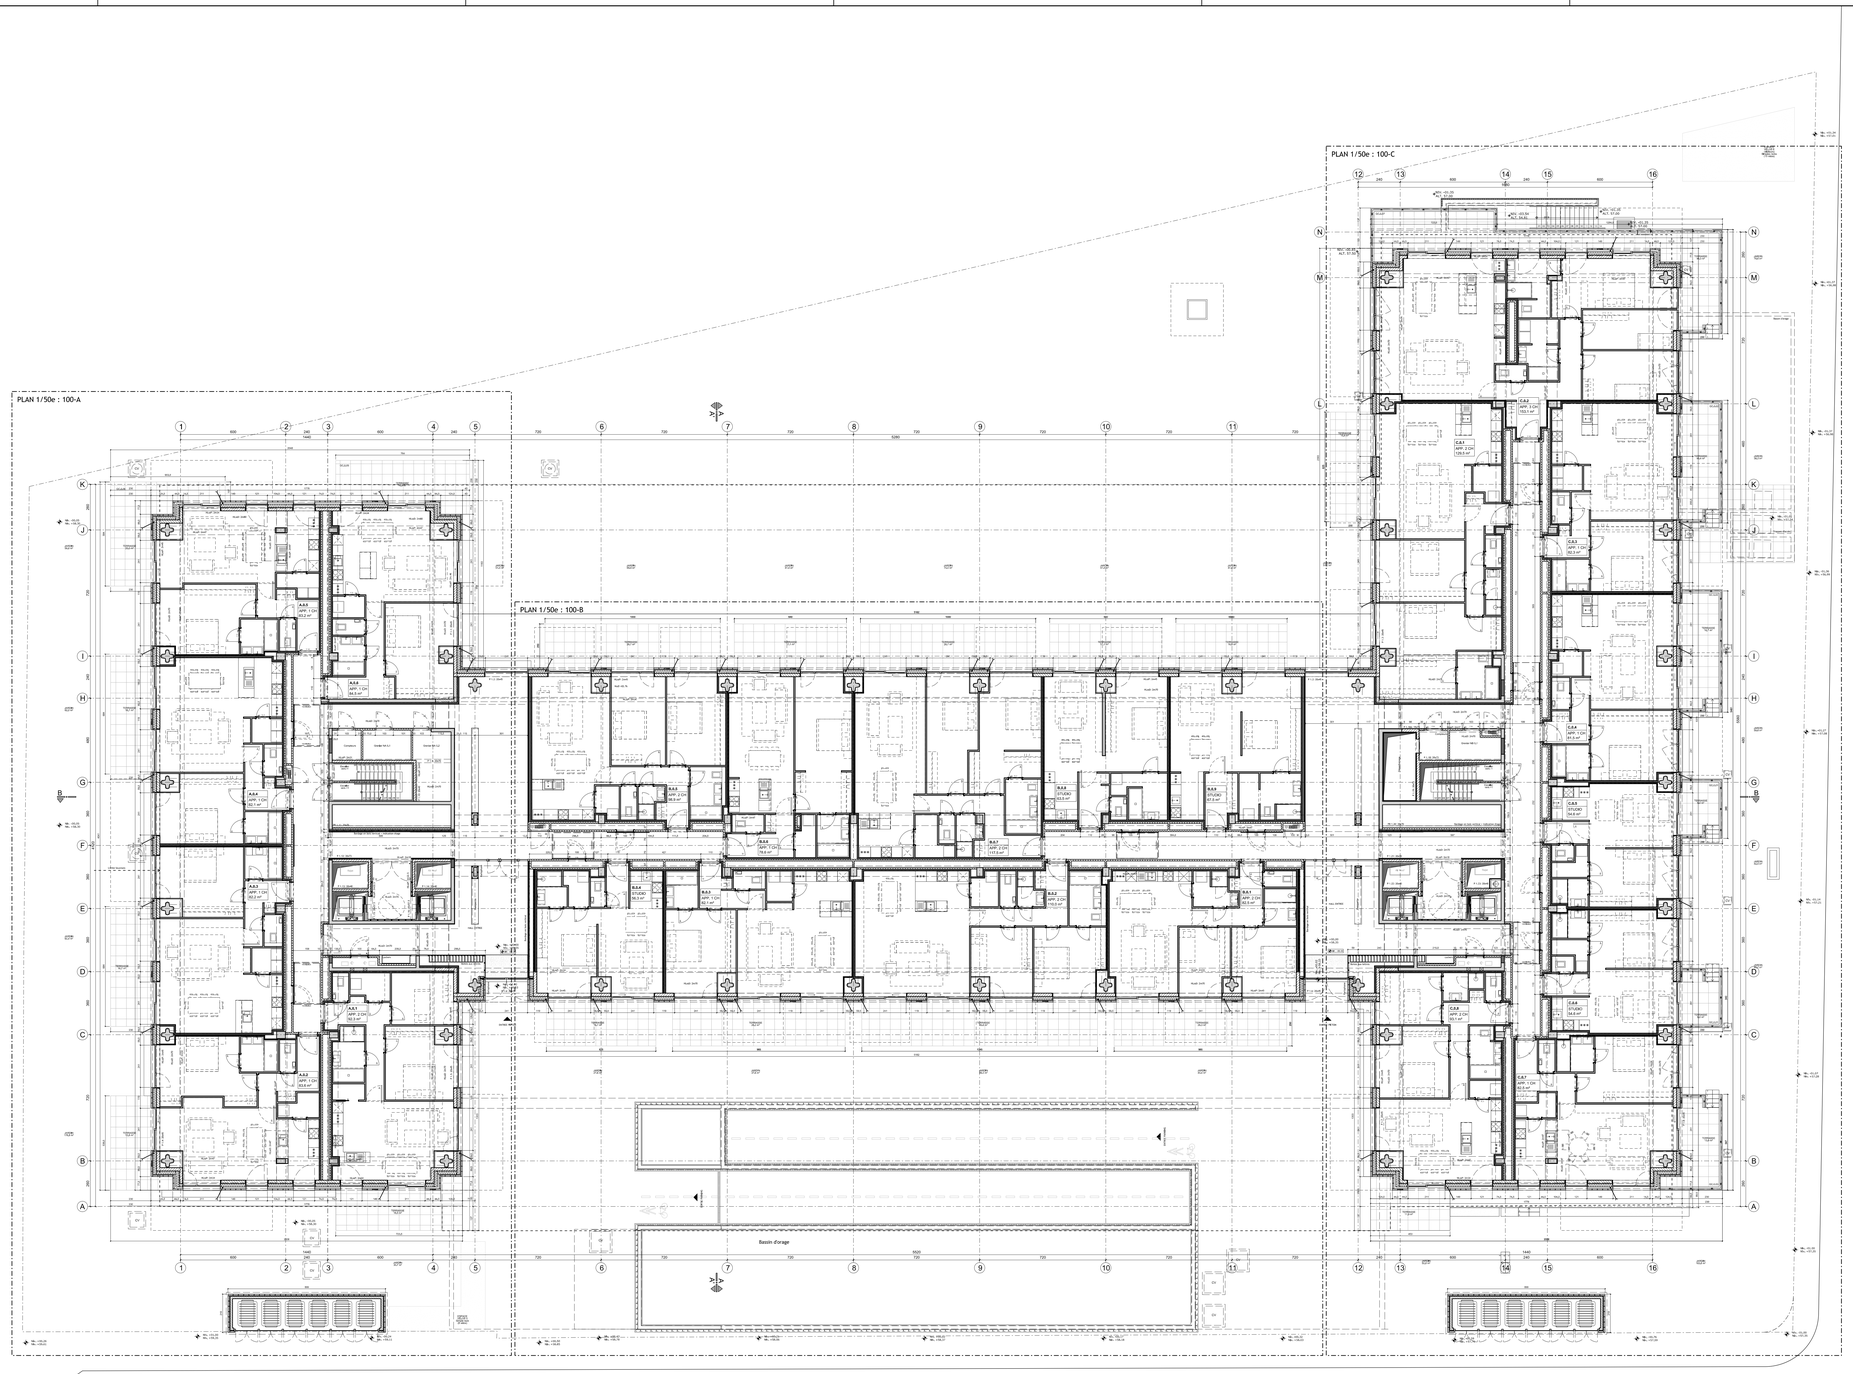

NUMEROTATION DES LOCAUX

X.1.2|BU|12

- NUMERO DU LOCAL
- AFFECTATION
- ALE.ETAGE.UNITE

	B : BUREAUX	GE : GROUPE ELECTROGENE	S : SAS
	BU : BUANDERIE	GR : GRENIER	SA : SAS ASCENSEUR
	CA : CAVE	GZ : LOCAL GAZ	SB : SALLE DE BAIN
	CB : COMPTEUR CAVES	HA : HALL ASCENSEUR	SD : SALLE DE DOUCHE
	CF : CHAUFFERIE	HE : HALL ENTREE	SE : SEJOUR
	CO : COULOIR	HJ : HALL DE JOUR	SF : SAS ESCALIER DE SECOURS
	CU : CUISINE	HL : HALL LOGEMENT	SI : SAS INCENDIE
	CU : CUISINE	LC : LOCAL COMPTEURS	ST : SAS TECHNIQUE
	DB : DEBARAS	LE : LOCAL ELECTRIQUE	VE : LOCAL VELOS
	DE : DEVIDOIR	LP : LOCAL POUBELLES	WC : TOILETTE SEPAREE
	DR : DRESSING	LV : LOCAL VENTILATION	WT : LOCAL COMPTEURS EAU
	E : ENTREPOT	M : LOCAL MECANIQUE	
	EN : ENTRETIEN	PA : PARKING	
	GA : BOX GARAGE	PO : LOCAL POUSSETTES	

S02 : 2e SOUS-SOL
S.1 : 1er SOUS-SOL
R.X : REZ-DE-CHAUSSEE
1.X : 1er ETAGE
2.X : 2e ETAGE
3.X : 3e ETAGE

LEGENDE DES FINITIONS

SOL MUR PLAFOND

- FINITION
- HAUTEUR LIBRE
- SYNTHESE
- SUPPORT
- INV. FINI
- FINITION

B : NOUVEAU BETON	FM : PLAF. SUS. FIBRE MINERALE	PR : PEINTURE DE PROPRETE
BE : BETON EXISTANT	G : PLAF. SUS. PLAQUES DE PLATRE	PS : PEINTURE STRUCTURE
BB : BLOCS DE BETON	GA : PLAF. SUS. PLAQUES DE PLATRE +	MS : MARQUAGE AU SOL/MURS
BC : CARRELAGE	GM : PLAF. SUS. METAL	VE : VERNIS/CIRE
BP : BLOCS DE PLATRE	GP : PLAF. SUS. PLAQUES DE PLATRE	ST : STRATIFIE
CA : CARRELAGE	PERFOREES + ISO. ACOUSTIQUE	
CE : CARRELAGE CERAME	M : PLAF. SUS. METAL	
EH : ENDUIT (PLAFONNAGE)	PL : PLAFONNAGE	
EP : PEINTURE EPOXY	PP : PRE-PEINT	
FA : FAIENCES	PT : PEINTURE	
LA : LATTIS + ISO. ACOUSTIQUE		

LEGENDE DES MATERIAUX DE FACADE

1. BRIQUE DE SAIGNER TYPE MORETUS
2. ELEMENT EN ALUMINIUM ANODISE C34
3. CHASSIS EN ALUMINIUM ANODISE C34
4. GARDE-CORPS VITRE
5. TRIPLE VITRAGE
6. DOUBLE VITRAGE
7. SOUBASSEMENT EN BETON ARCHITECTONIQUE TEINTE SIMILAIRE TEINTE BRIQUE
8. ENDUIT SUR ISOLANT

LEGENDE GENERALE MATERIAUX

- BETON EXISTANT
- BETON NEUF
- MACONNERIE EN BLOC DE PLATRE
- MACONNERIE EN BLOC DE BETON
- ISOLATION SOUPLE
- ISOLATION RIGIDE
- CLOISON ET CONTRE-CLOISON EN PLAQUE DE PLATRE ISOLEE
- PAREMENT FACADE EN BRIQUES

Parement
Parement maçonnerie en pierre naturelle
0.00 (+ 10.00 cm)
(+ 10.00 cm) 0.00 (+ 10.00 cm)
(+ 10.00 cm) 0.00 (+ 10.00 cm)

Rue du Moulin à papier / Avenue Ch. Lemaire
1160 Auderghem

Cadastre 4242

Parc Seny 447

Immeuble de logements AB

Filir

Modifications	Date
A	
B	
C	
D	
E	
F	
G	
H	
I	
J	
K	
L	
M	
N	
O	
P	
Q	
R	
S	
T	
U	
V	
W	
X	
Y	
Z	

MO	maître de l'ouvrage	BRUSSELS EAST REAL ESTATE Anciennement SPI PARC SENY Rue de la Régence, 58 - 1000 Bruxelles T +32 2 423 53 11 / F +32 2 423 53 01
ARC	architecture	ARCHI 2000 Avenue du Prince d'Orange, 6 - 1000 Bruxelles T +32 2 375 87 30 / F +32 2 375 94 68 info@archi2000.be - www.archi2000.be
ICS	stabilité	Setesco sa Avenue Maurice, 50 / 57 - 1050 Bruxelles T +32 2 648 91 60 - F +32 2 648 00 73 bxl@setesgroup.be - www.setesco.be
ICT	techniques spéciales - PEB	CES nv Brusselsesteenweg, 290 - 1731 Asse T +32 2 452 20 02 info@ces-web.be - www.ces-web.be
ICA	acoustique	Venac bureau d'études Rue des Intéressants 49 b (0201) - 1070 Bruxelles T +32 2 523 34 34 - F +32 2 523 34 35 venac@venac.be - www.venac.be
ARP	architecte paysagiste	Landscape Design Partnership sprl Rue du Serpentin, 31 - 1050 Bruxelles T +32 2 672 34 29 bcapelle@landscapedesign.net - www.landscapedesign.net
CSS	coordination sécurité	Bureau PS2 Rue Auguste Lannoye, 60/201 - 1420 Braine-l'Leud-Lillois T +32 10 65 93 12 info@bureaups2.be - www.bureaups2.be

copyright Archi 2000

PARC SENY

A B C

RUE LEMAIRE

RUE DU MOULIN A PAPIER

Echelle	1/100	Format	A0+ 841x1189	Date	13/01/2020

phase	DOSSIER AS-BUILT						
titre	Situation projetée Niveau 00						
ARC Architecte	Bâtiment	AB Phase	PR Chapitre	100 Numéro	Cartouche	Indice	